A VERIFICAR EN OBRA / CON EL ORIGINAL

1. Retiro de frente: 1,50 m medido a escala; el plano no trae la cota.
2. Hall PB: lei 2,05 de profundidad (podria decir 3,05).
3. Living: elemento junto a la medianera (hogar / guardarropa?) sin identificar.
4. Paño angosto al lado de la puerta C: lo tome como carpinteria I (0,35).
5. Paso antecocina - lavadero: tipo y ancho de puerta ilegibles.
6. Porton B': lo ubique a 6,60 m de la linea municipal.
7. Placares entre hall y antecocina: profundidades estimadas.
8. La planta alta da 0,45 m mas larga que la baja: vuela atras, o la cocina mide 4,65 y no 4,35?
9. Terraza: largo sin cota (dibujada del baño al fondo); vuela 0,45 sobre el pasillo.
10. Escalera: recorrido esquematico (ancho 0,85). Contar escalones en obra.
11. Medianeras: ejes y espesores (0,30) a confirmar; muro derecho dibujado solo en parte.

PLANILLA DE CARPINTERIA


PUERTAS

A	madera 0,80 x 0,70 (porton de cerco)
B / B'	madera 2,26 x 2,10
C	madera 0,80 x 2,10
D	madera 0,70 x 2,10
E	madera 0,70 x 2,10
F	madera 1,00 x 1,90
G	madera 1,60 x 1,90
H	madera 0,60 x 1,50
I	madera 0,35 x 1,90

VENTANAS


J	madera 1,50 x 1,30
K	madera 2,00 x 1,30
L	madera 1,95 x 1,10
M	madera 1,20 x 1,10
N	hierro 1,80 x 0,80
O	hierro 0,80 x 0,50

HUMBERTO 1o 958 - PUNTA ALTA
Redibujo del plano municipal aprobado en 1965 (escala original 1:100)
Lote F, manzana 60 - 8,66 x 35,00 m - Sup. terreno 303,10 m2
Unidades del dibujo: METROS. Redibujado desde las cotas escritas;
NO es un relevamiento: medir en obra antes de usarlo para obra o compras.

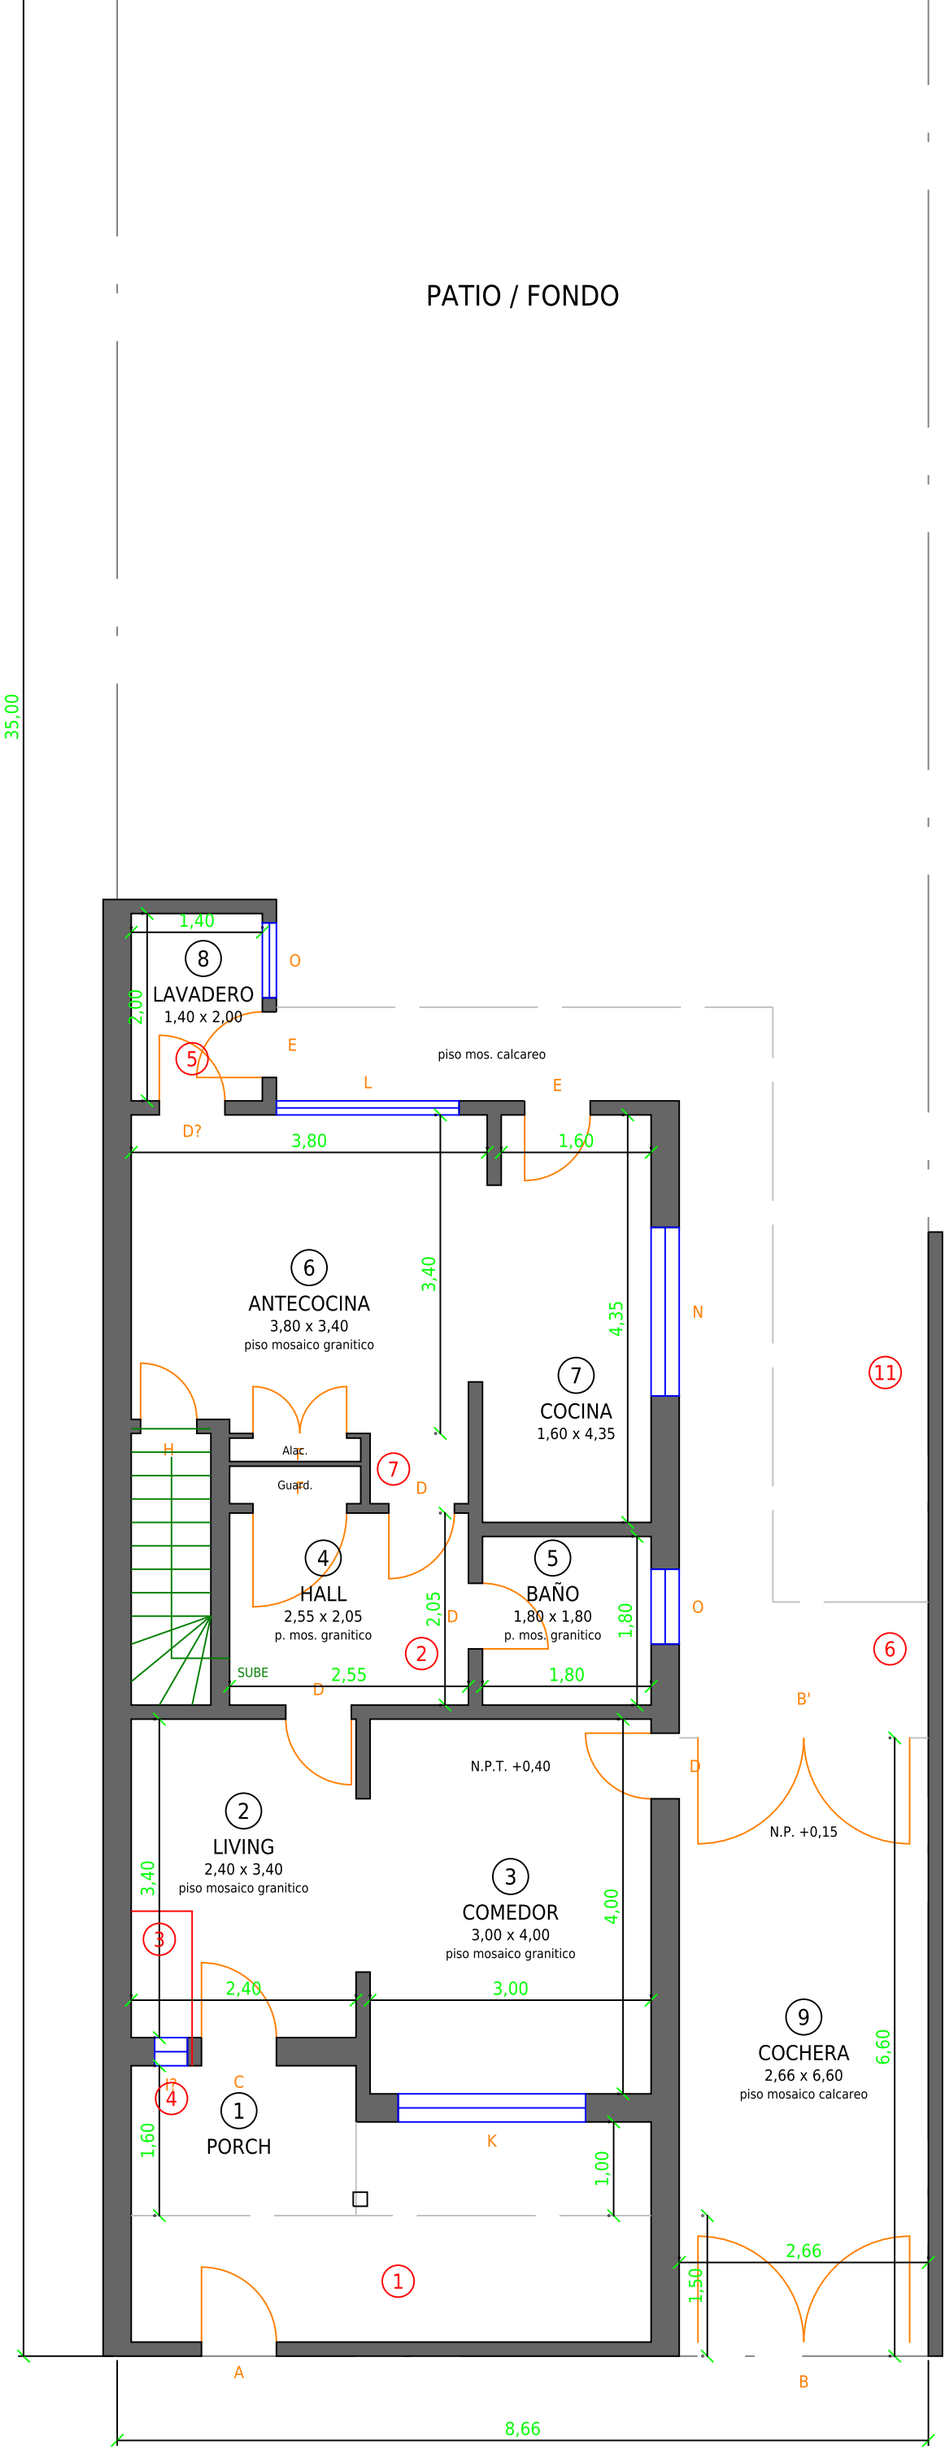

LINEA MUNICIPAL - CALLE HUMBERTO 1o

PLANTA BAJA

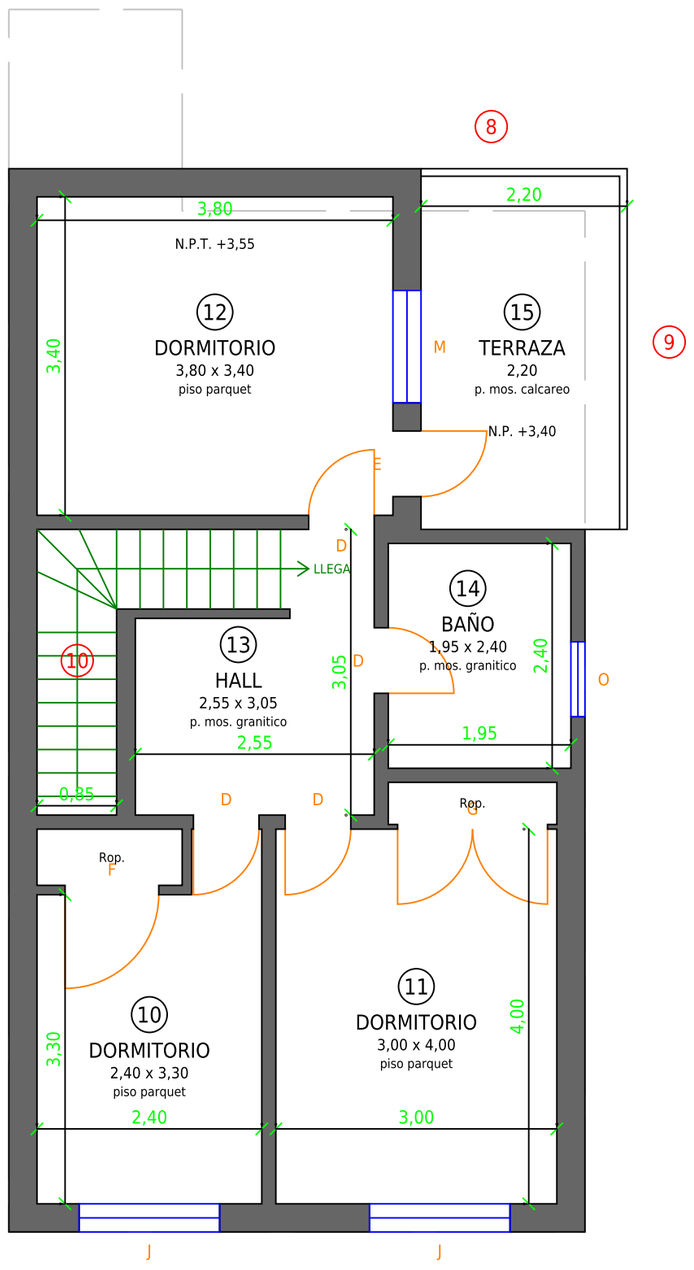

(linea de trazos: contorno de planta baja)

PLANTA ALTA